

Barndo Florida ~2400 SF

Led the complete architectural design and documentation of a 2400 SF custom residential barndominium project in Florida, ensuring compliance with local building codes and regulations. (Good general overview, highlights leadership and compliance).


Developed comprehensive architectural drawings, including detailed floor plans (First Floor & Mezzanine), exterior renderings, and spatial layouts, utilizing advanced BIM/CAD software. (Highlights specific deliverables and software proficiency like Archicad, as evident in the drawing).

Managed the design process from conceptualization through detailed construction documentation for a multi-story residential structure, optimizing space utilization and aesthetic appeal. (Focuses on the full lifecycle and design quality).

Collaborated with clients to translate design vision into detailed architectural plans, incorporating specific spatial requirements such as garage, multi-level living areas, and integrated staircase design. (Emphasizes client interaction and detailed design).

Produced high-quality 3D visualizations and renderings (as shown in the exterior view) to facilitate client understanding and design approvals. (Highlights visualization skills, aligning with your CV's mention of Lumion/V-Ray/Twinmotion).

Executed precise technical drawings and layouts for all levels, demonstrating meticulous attention to detail in structural integration and spatial planning. (Focuses on technical accuracy and attention to detail).

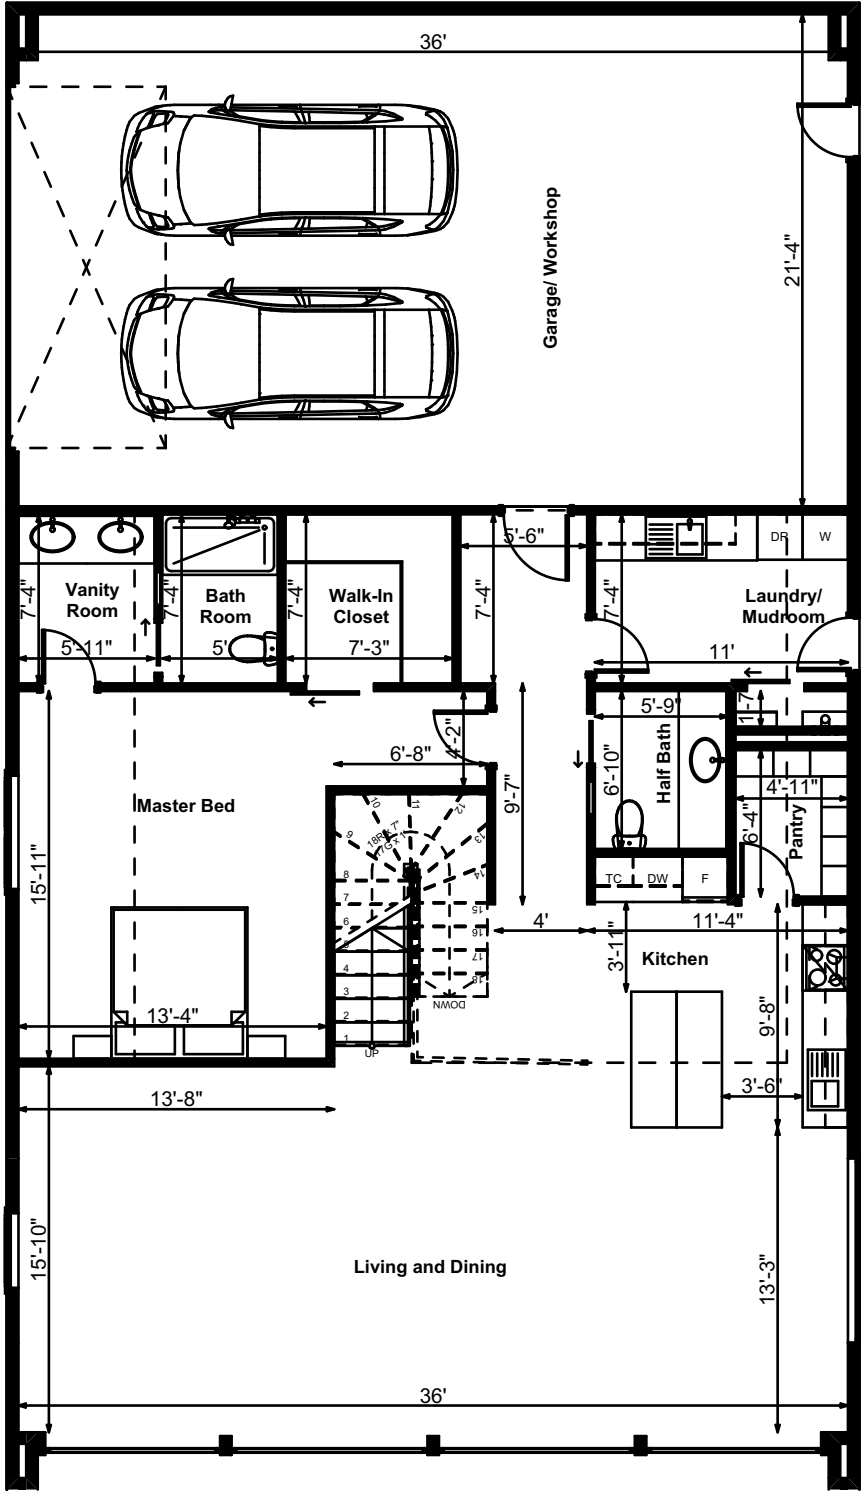


First Floor

1:100



Exterior

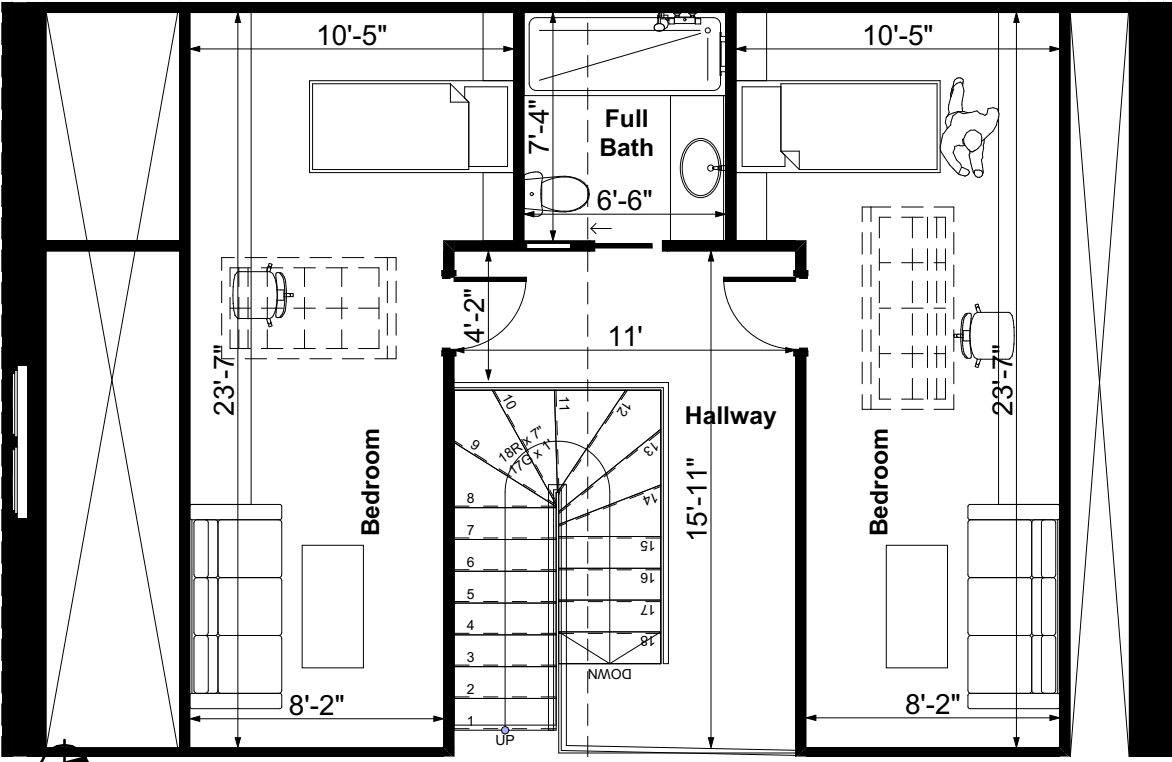

Mezzanine Floor





NOT FOR CONSTRUCTION

Project Title:
Barndominium

Layout ID:
A.01.2

Drawing Layout:
A-04 Landscape

Drawing Subset:
Visualization





NOT FOR CONSTRUCTION

Project Title:
Barndominium

Layout ID:
A.01.3

Drawing Layout:
A-04 Landscape

Drawing Subset:
Visualization

