



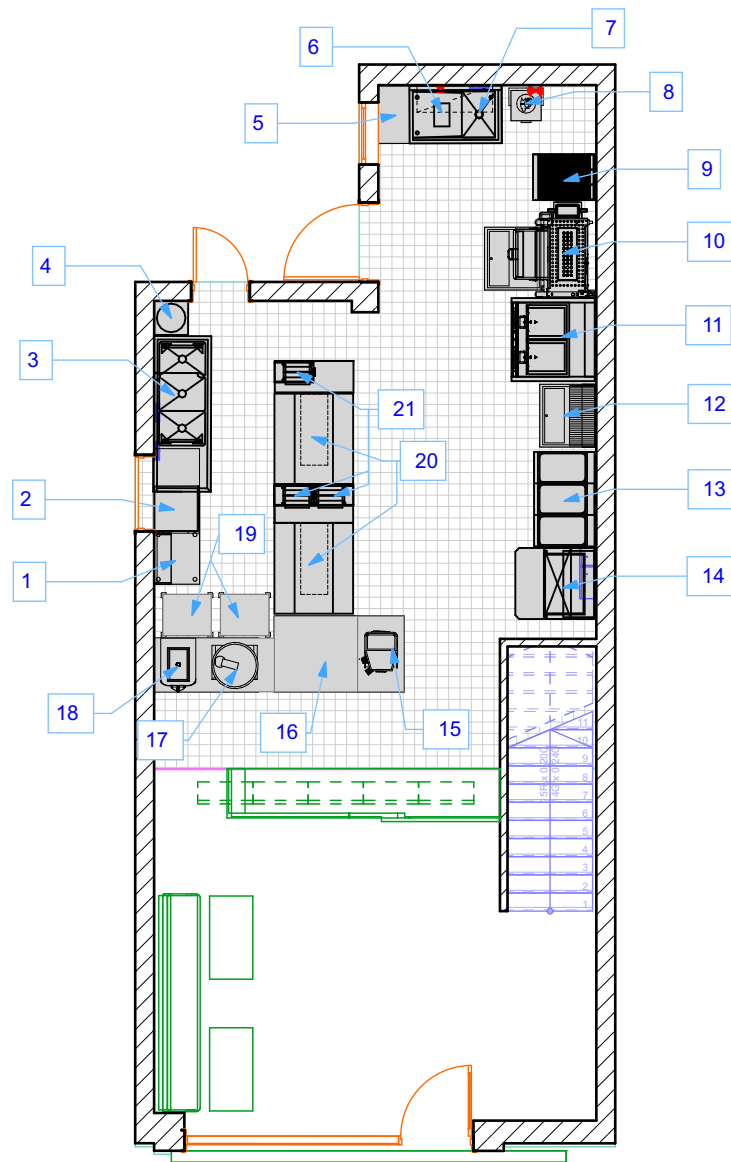


Label number	Description
1	Shelf
2	Dish washer
3	3 basin sink
4	Hand wash sink
5	Prep table
6	Slide freezer
7	Sink
8	Recycle bin
9	Chargrill
10	Broiler
11	Griddle
12	Upright Freezer
13	3 phase fryer
14	Dump fryer
15	Espresso machine
16	Burger chute
17	Drink dispenser
18	Icecream machine
19	Bun rack
20	Food warmer
21	Toaster

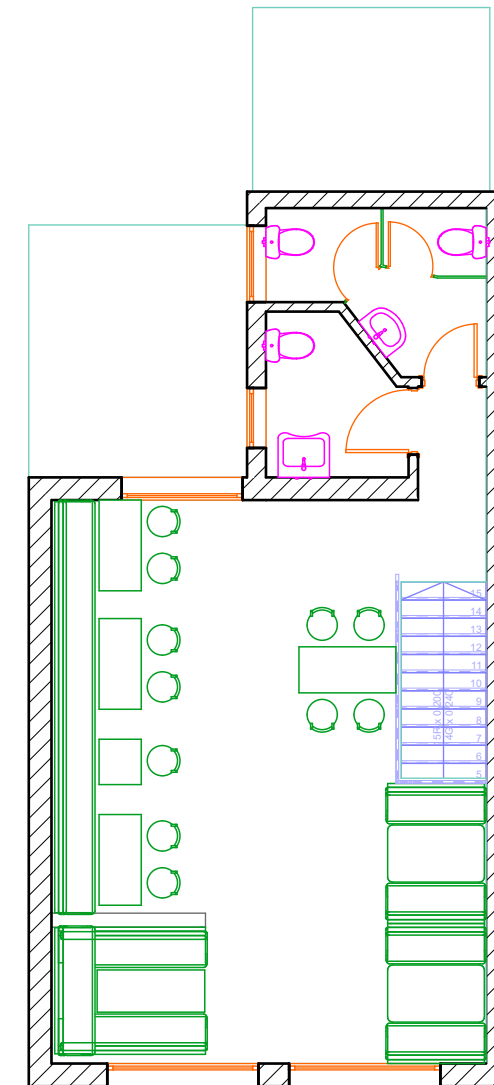

0. Ground Floor 1:100

1. First Floor 1:100



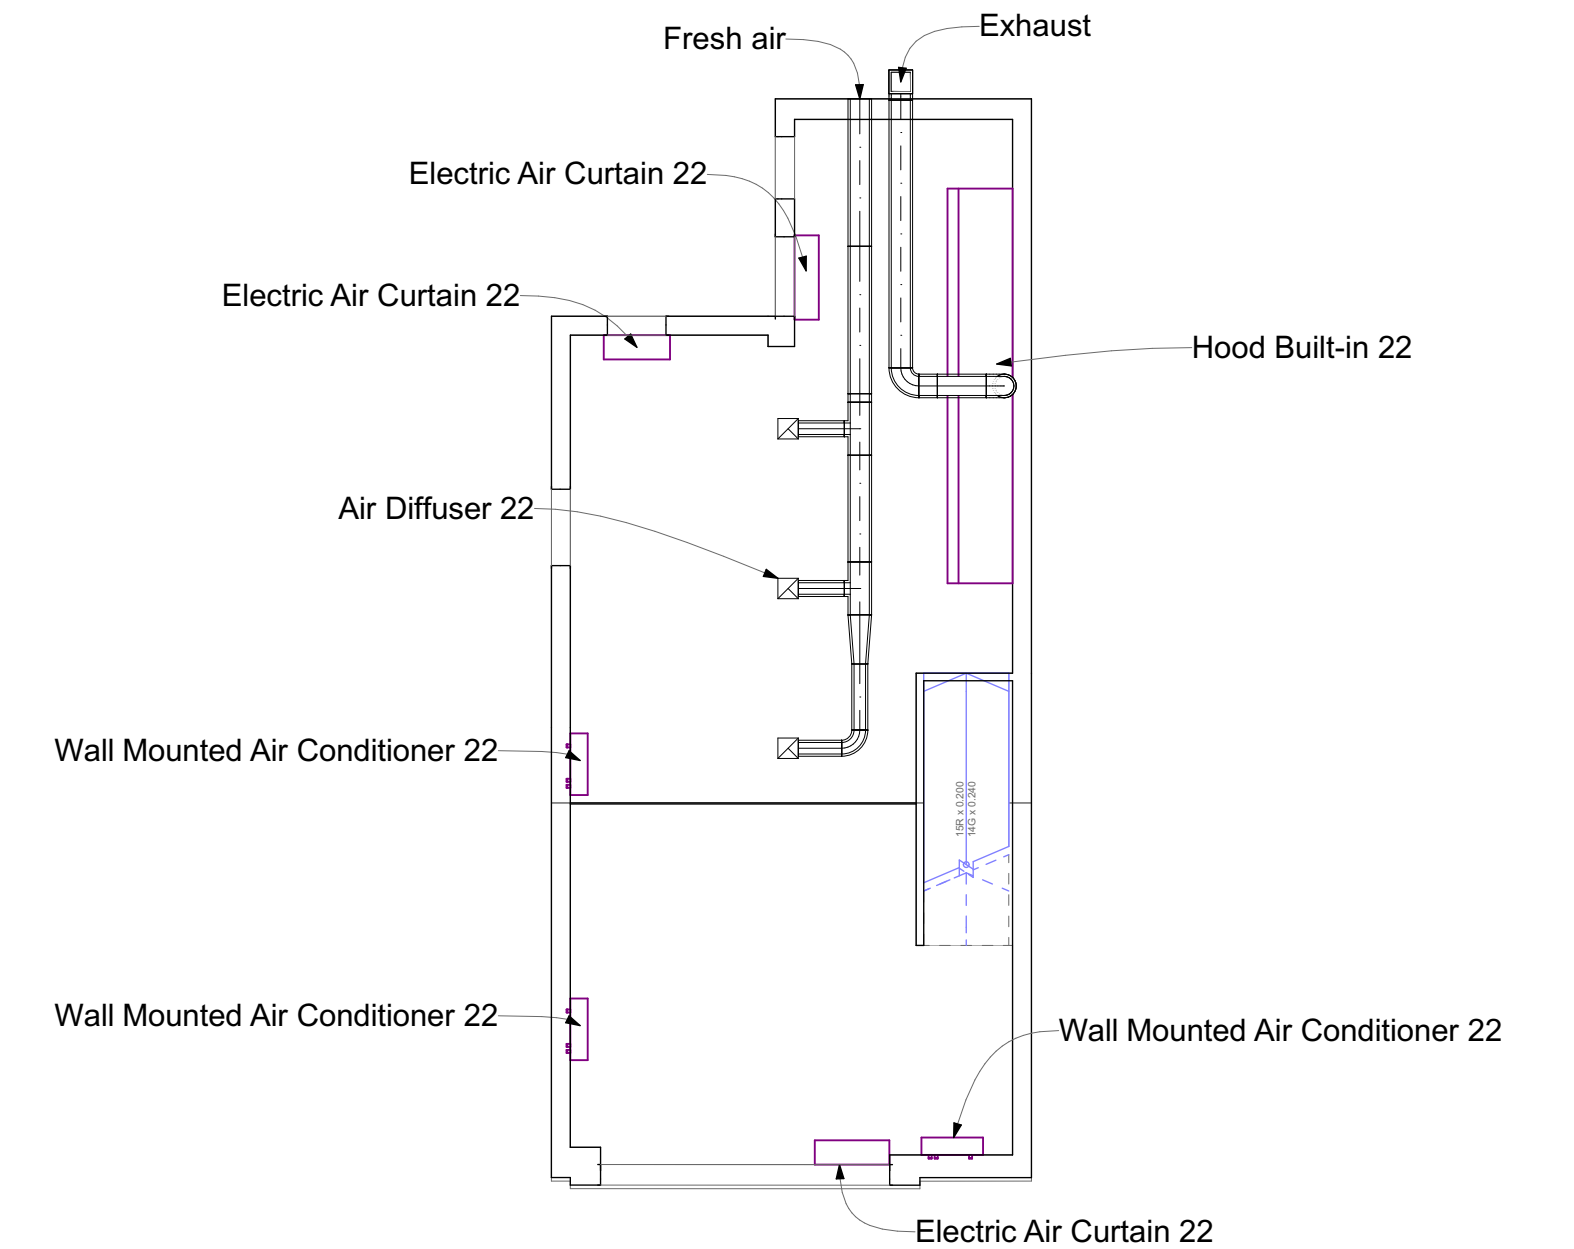

0.

Ground Floor

1:100


Project Title:
Slamburger

Drawing subset:
HVAC Plans

ID:A.02 Ground Floor

Arslan Qaiser
Architecture Design Consultant
arslan.qaiser1991@gmail.com



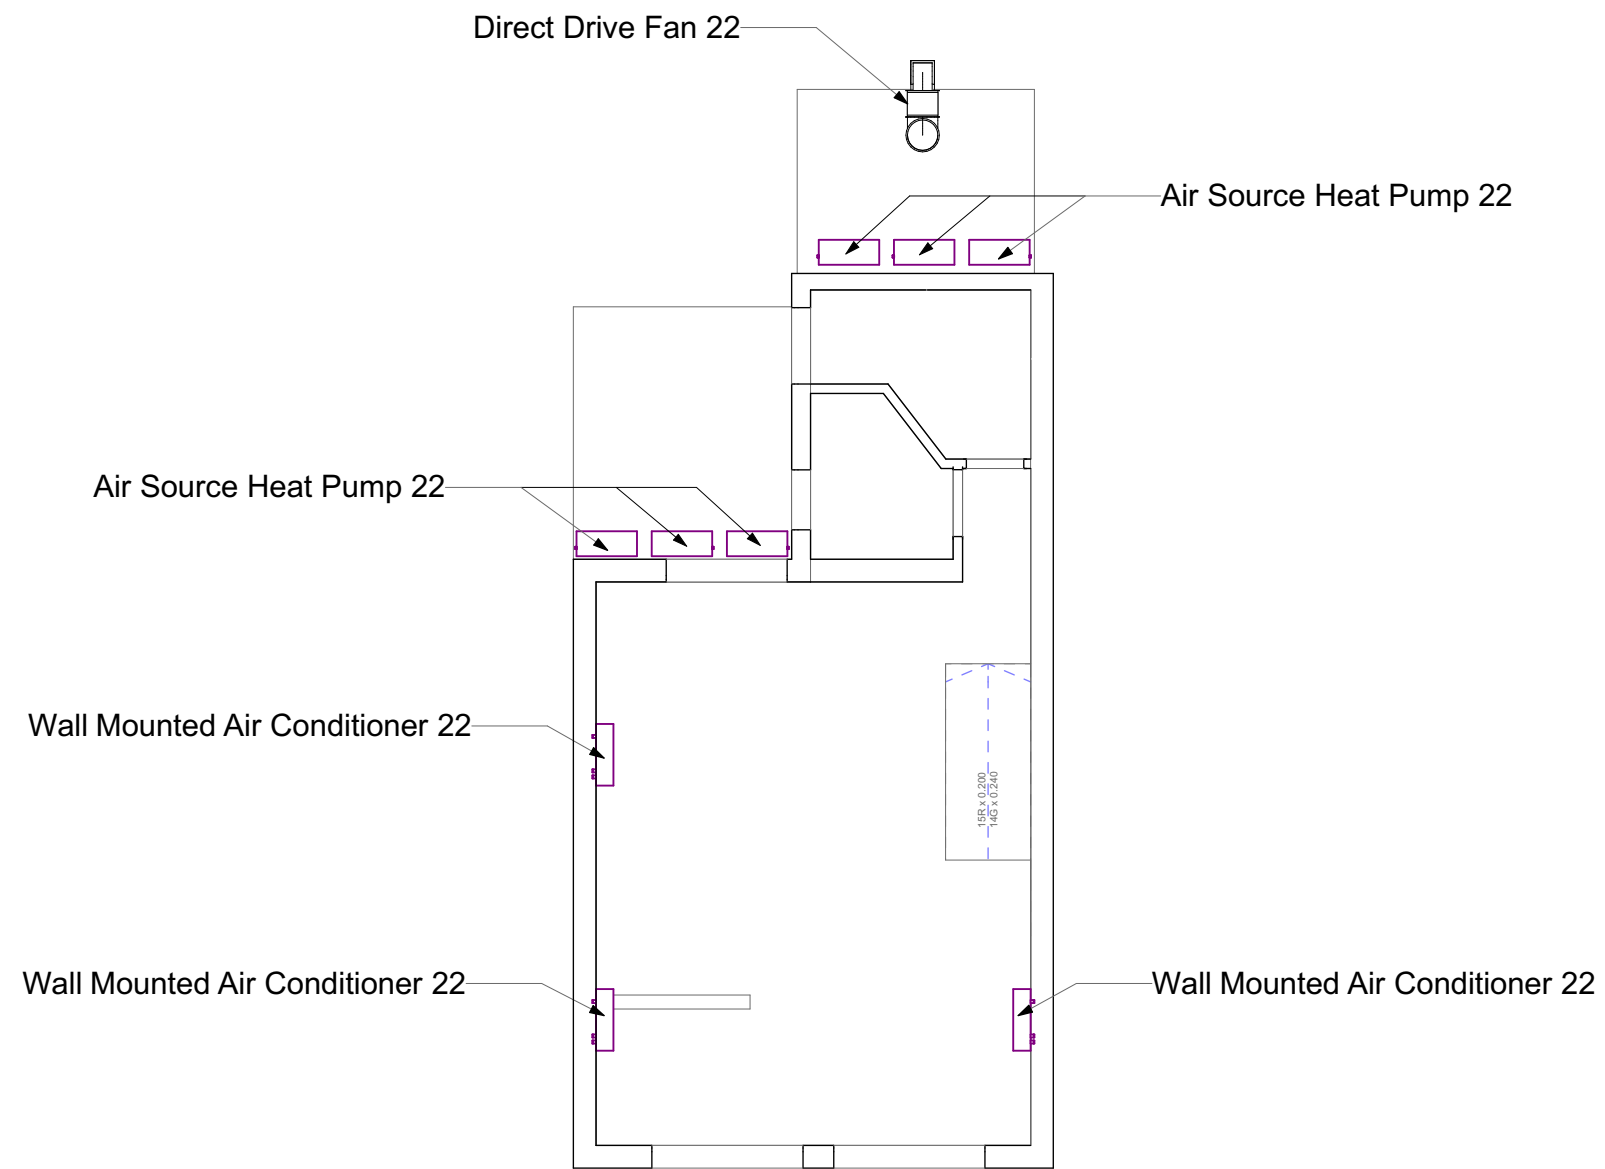

1.

First Floor

1:100


Project Title:
Slamburger

Drawing subset:
HVAC Plans


ID:A.03 First Floor

Arslan Qaiser
Architecture Design Consultant
arslan.qaiser1991@gmail.com




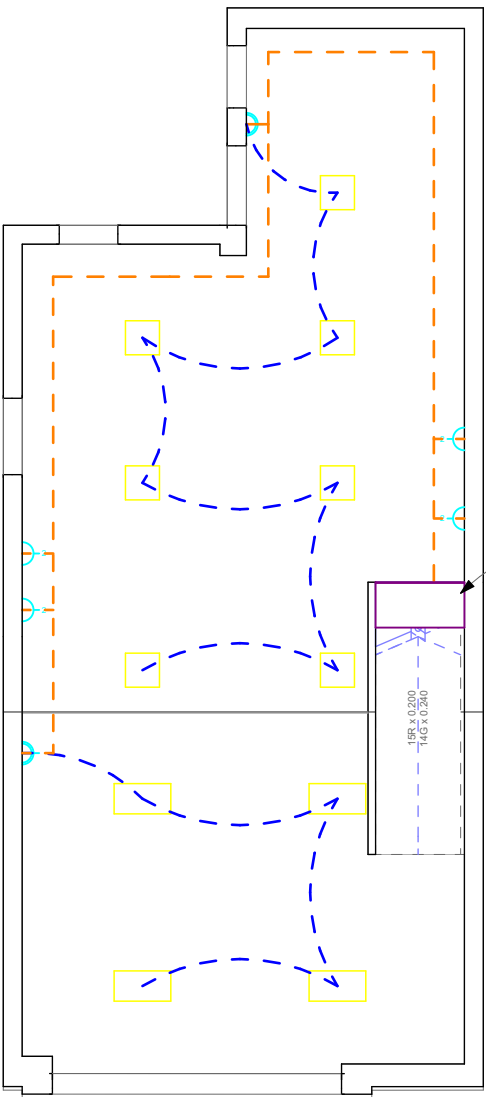


Circuit Breaker Switchboard 22

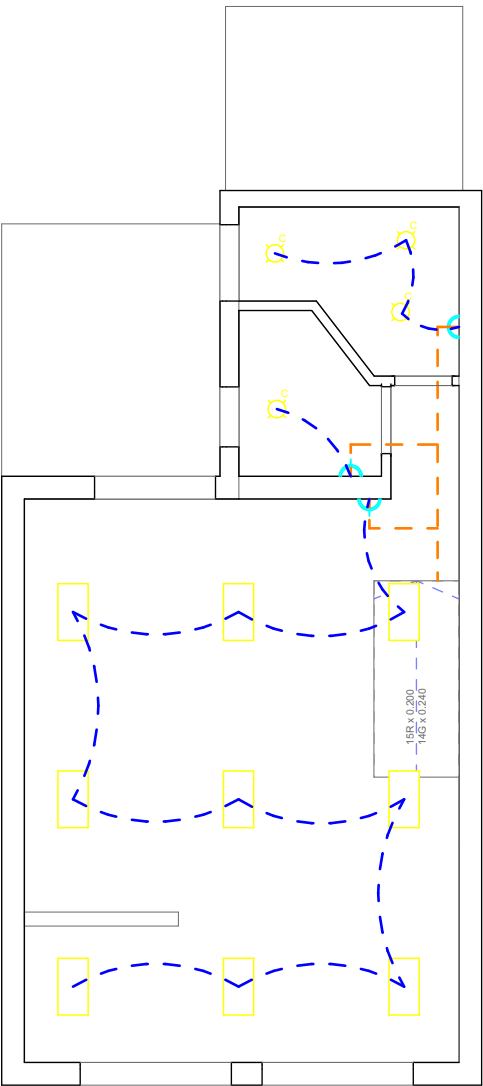

Electrical devices Legend				
Home Story Name	Library Part Name	Quantity	2D Plan Preview	Related Zone Name
Ground Floor				
	Ceiling Lamp 22	4		Lower Dining
	Ceiling Lamp 22	7		Kitchen
	Socket Outlet 2 Gangs 22	4		Kitchen
	Socket Outlet Multiple 2 Gangs 22	1		Kitchen
	Socket Outlet Multiple 2 Gangs 22	1		Lower Dining
First Floor				
	Ceiling Lamp 22	9		Upper Dining
	Recessed Spot 22	1		Womens Bathroom
	Recessed Spot 22	3		Mens Bathroom
	Socket Outlet Multiple 2 Gangs 22	1		Mens Bathroom
	Socket Outlet Multiple 2 Gangs 22	1		Upper Dining
	Socket Outlet Multiple 2 Gangs 22	1		Womens Bathroom

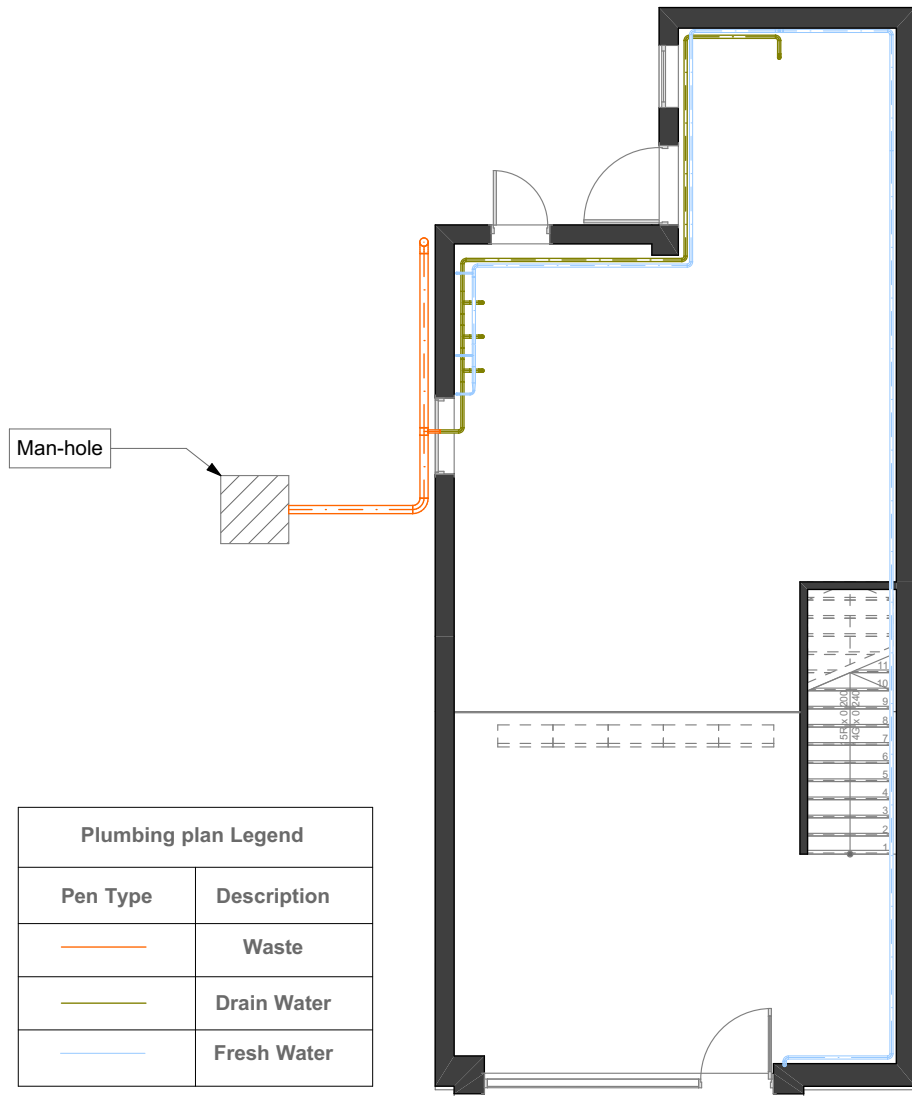


0. Ground Floor 1:100

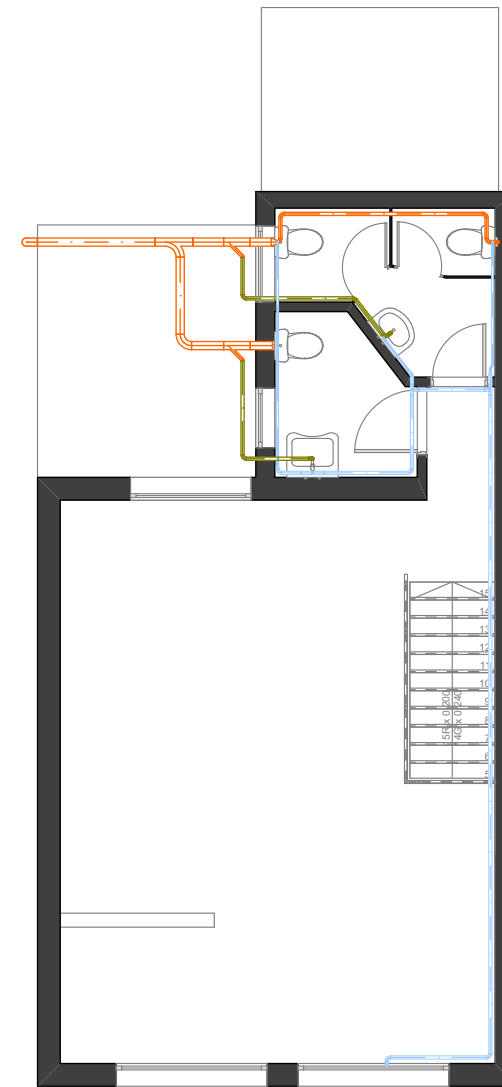


1. First Floor 1:100




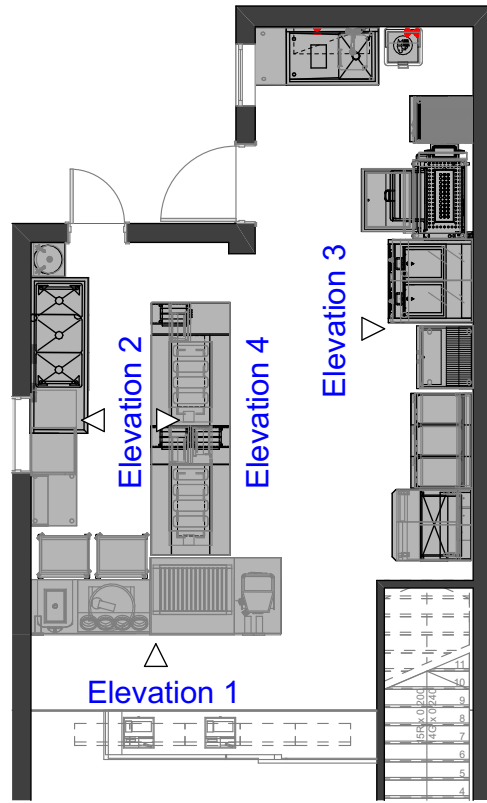

0. Elevations plan 1:100

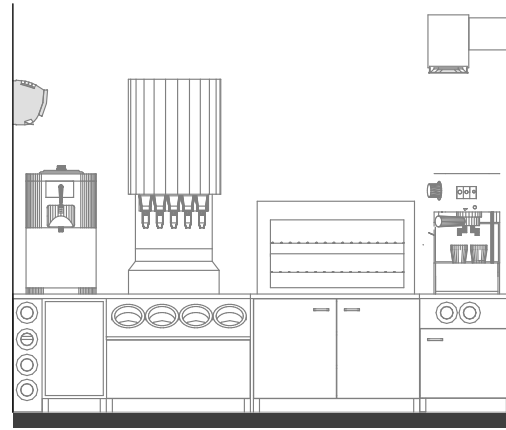


1 Elevation 1 1:50

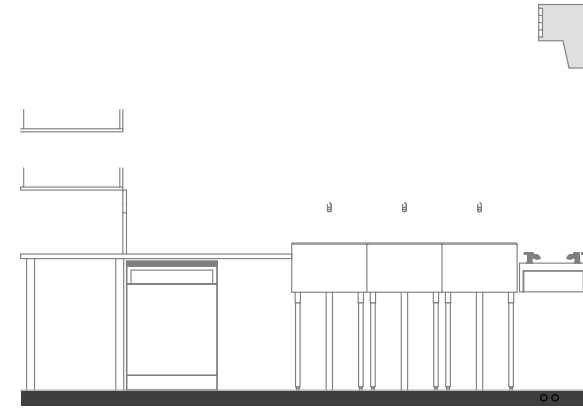

3 Elevation 2 1:50



2 Elevation 3 1:50

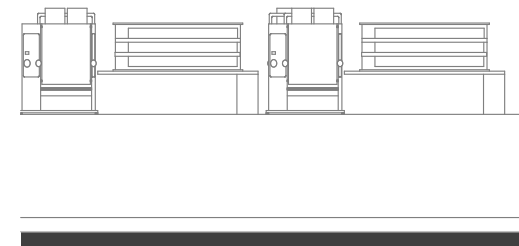

4 Elevation 4 1:50

Project Title:
Slamburger

Drawing subset:
Elevations

ID:A.06 Elevations plan,
Elevation 3, Elevation 1,
Elevation 2, Elevation 4

Arslan Qaiser
Architecture Design Consultant
arslan.qaiser1991@gmail.com





Project Title:
Slamburger

Drawing subset:
Renderings

Arslan Qaiser
Architecture Design Consultant
arslan.qaiser1991@gmail.com





Project Title:
Slamburger

Drawing subset:
Renderings

Arslan Qaiser
Architecture Design Consultant
arslan.qaiser1991@gmail.com





Project Title:
Slamburger

Drawing subset:
Renderings

Arslan Qaiser
Architecture Design Consultant
arslan.qaiser1991@gmail.com





Project Title:
Slamburger

Drawing subset:
Renderings

Arslan Qaiser
Architecture Design Consultant
arslan.qaiser1991@gmail.com





Project Title:
Slamburger

Drawing subset:
Renderings

Arslan Qaiser
Architecture Design Consultant
arslan.qaiser1991@gmail.com

