




Components by Elements					
Home Story Name	Element type	Materials	Measurments		
			Thickness (feet)	Area (Square feet)	Volume (cubic feet)
Footing					
	Column	Reinforced Concrete - Structural	1'-6"	---	101.25
	Column	Reinforced Concrete - Structural	1'	---	54.00
Basement					
	Column	Reinforced Concrete - Structural	1'-6"	---	337.50
	Column	Reinforced Concrete - Structural	1'	---	180.00
	Slab	Gravel	2"	2,325.17	381.43
	Slab	Reinforced Concrete - Structural	6"	2,533.88	1,266.94
	Slab	Tile - Floor		2,325.17	76.29
	Wall	Brick	5"	1,866.47	691.20
	Wall	Insulation - Plastic Hard	1"	2,091.35	250.12
	Wall	Masonry Block - Filler	5"	239.33	89.28
	Wall	Plaster - Gypsum		1,934.08	75.42
Wall	Reinforced Concrete - Structural	6"	1,989.24	954.90	
Ground Floor					
	Column	Reinforced Concrete - Structural	1'-6"	---	337.50
	Column	Reinforced Concrete - Structural	1'	---	180.00
	Slab	Gravel	2"	2,221.09	364.35
	Slab	Plaster - Gypsum		978.88	32.12
	Slab	Reinforced Concrete - Structural	6"	1,938.46	969.23
	Slab	Tile - Floor		1,060.04	34.78
	Slab	Tile - Floor	1"	1,161.05	76.18
	Wall	Masonry Block - Filler	5"	2,471.92	897.02
First Floor					
	Beam	Reinforced Concrete - Structural	1'	43.31	42.63
	Column	Reinforced Concrete - Structural	1'-6"	---	337.50
	Column	Reinforced Concrete - Structural	1'	---	180.00
	Slab	Gravel	2"	2,238.94	367.28
	Slab	Reinforced Concrete - Structural	6"	1,956.64	978.32
	Slab	Tile - Floor		2,238.94	73.46
	Wall	Masonry Block - Filler	5"	2,205.85	806.03
Second Floor					
	Column	Reinforced Concrete - Structural	1'	---	180.00
	Column	Reinforced Concrete - Structural	1'-6"	---	337.50
	Slab	Gravel	2"	2,233.03	366.31
	Slab	Reinforced Concrete - Structural	6"	1,998.77	999.38
	Slab	Tile - Floor		2,233.03	73.26
	Wall	Masonry Block - Filler	5"	2,380.63	867.86
Roof					
	Slab	Gravel	2"	2,272.00	372.70
	Slab	Gravel	1"	138.52	13.63
	Slab	Insulation - Fiber Hard	5"	138.52	54.54
	Slab	Membrane - Rainproof		138.52	2.27
	Slab	Membrane - Vapor Barrier		138.52	2.27

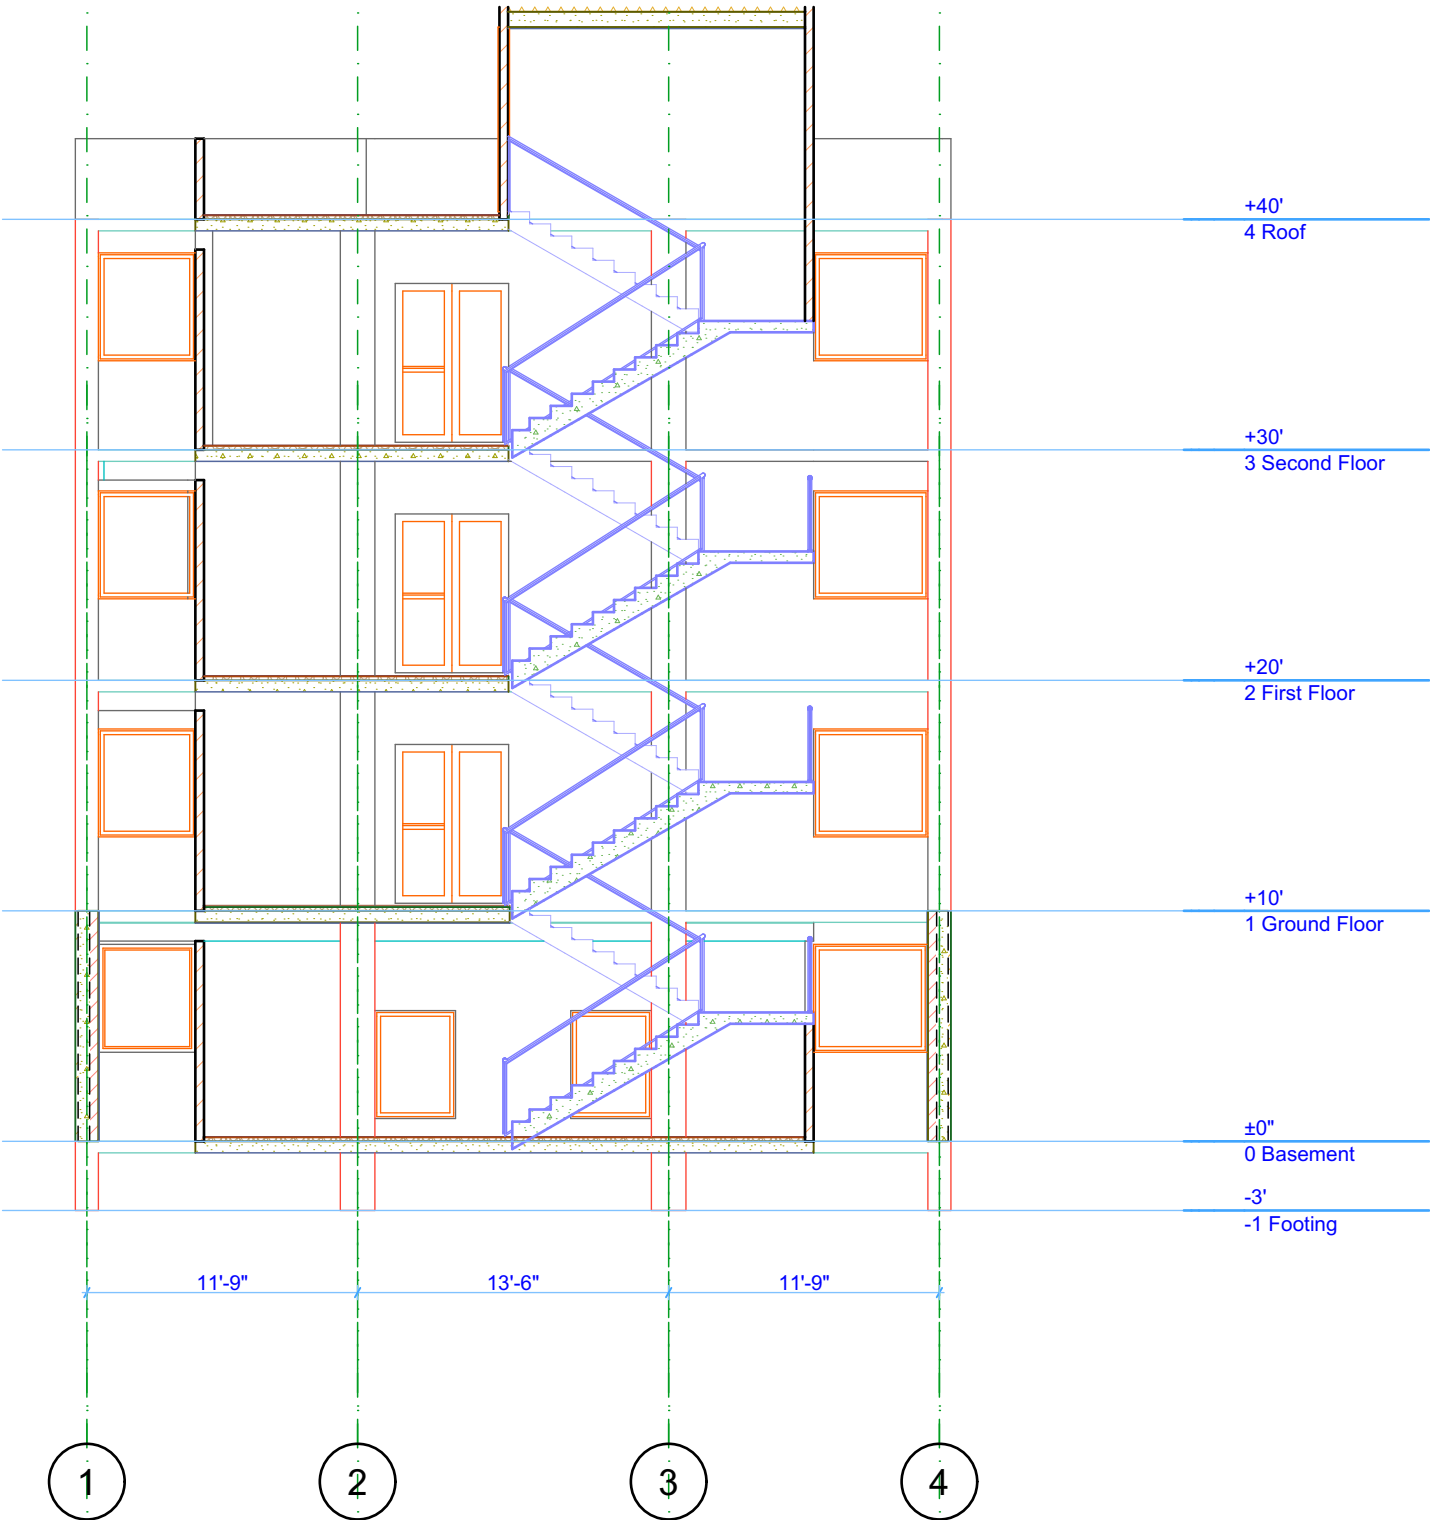

Building Section

S-01